


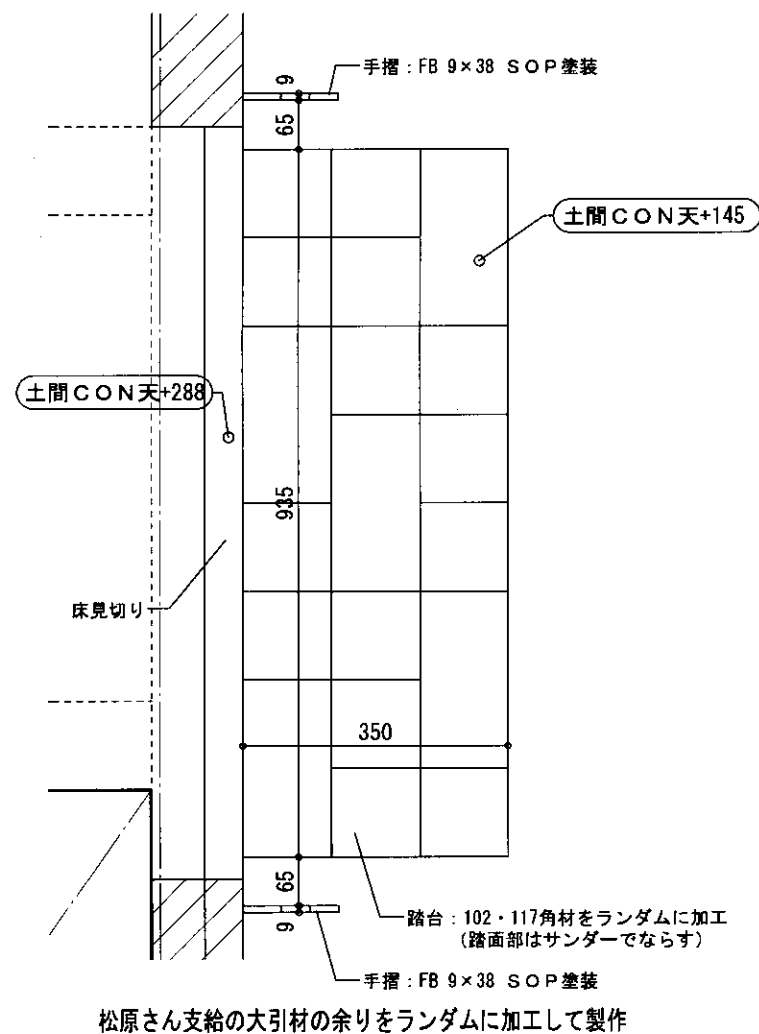


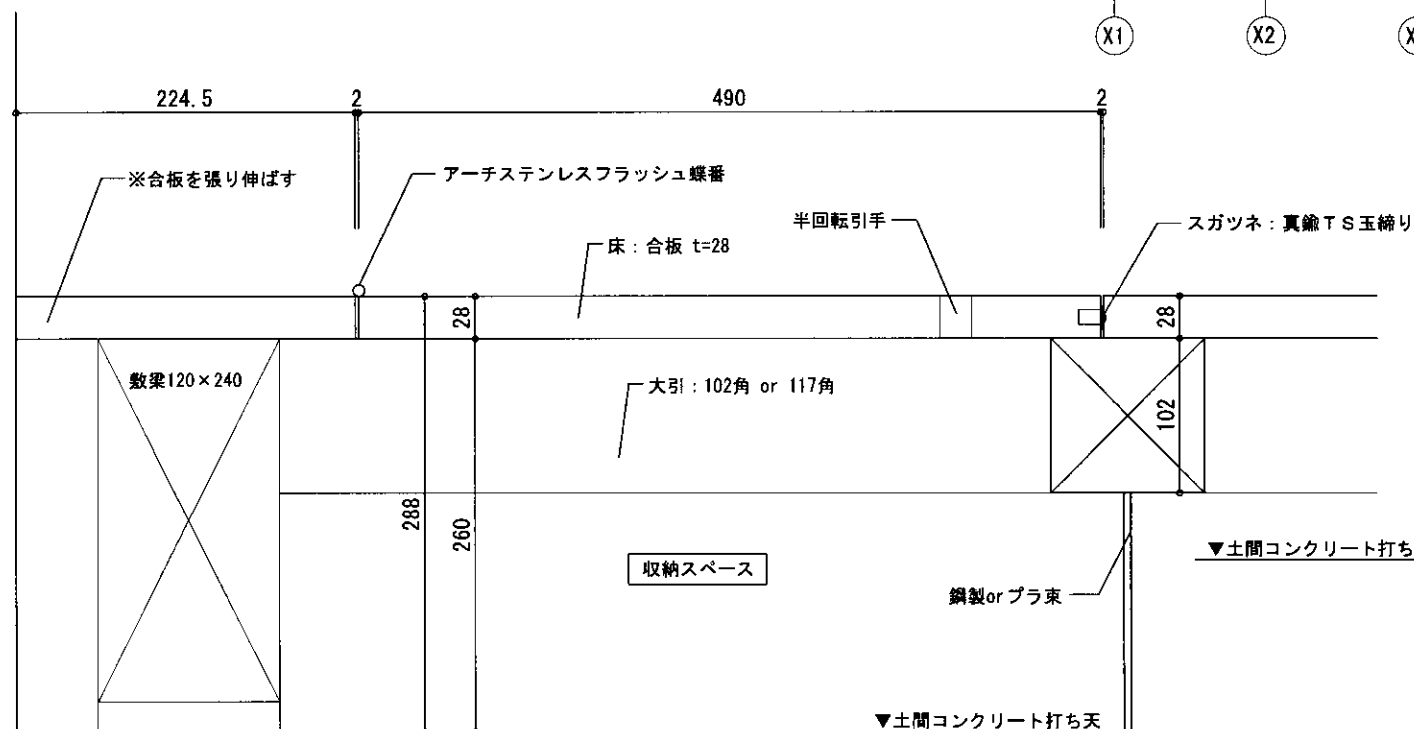

踏台詳細図 1/10

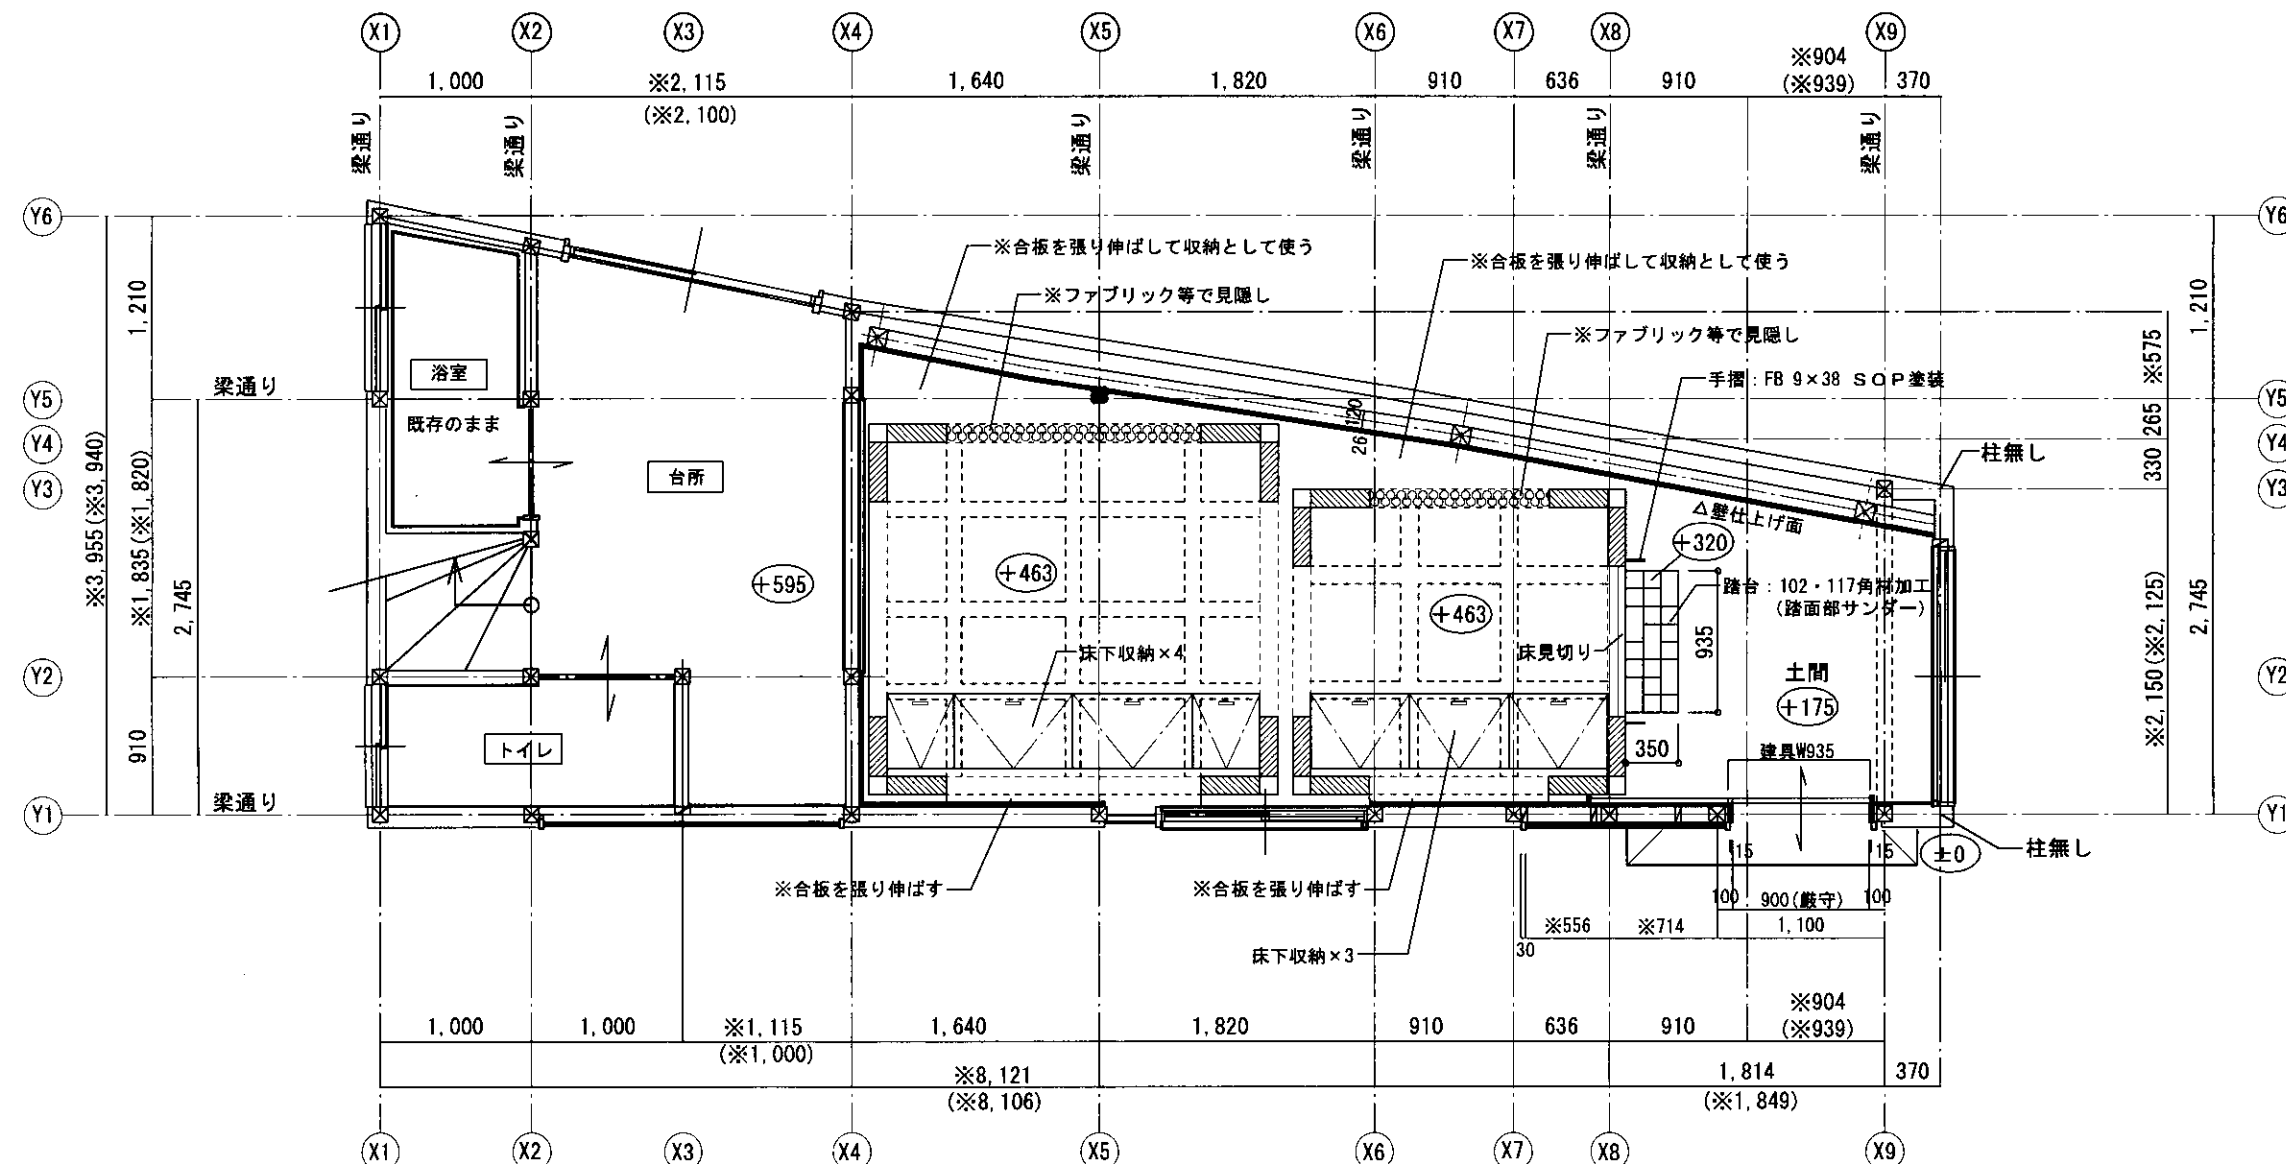

床下収納詳細図 1/5

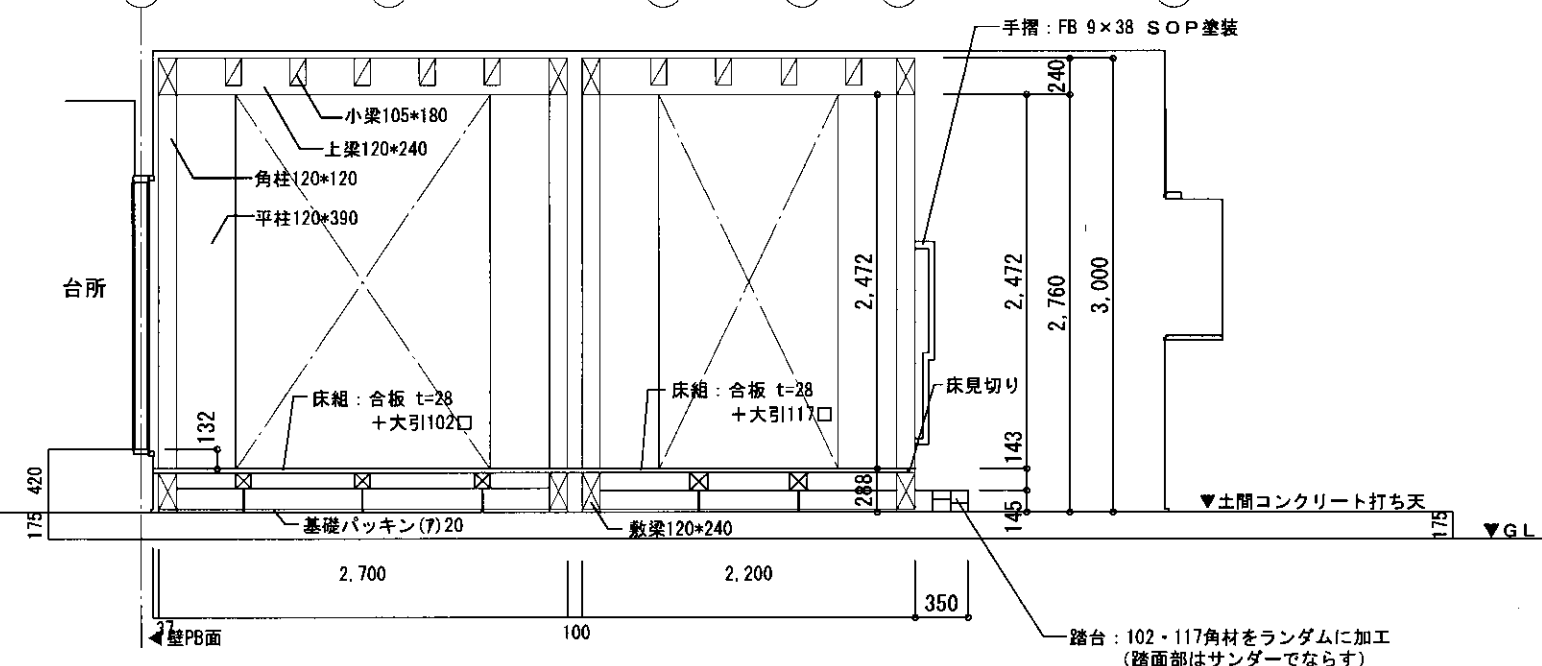

一般社団法人 岡山建築士会
倉敷支部会館 改築計画

工事名称

図面タイトル

床下収納計画図

no. 計画-13

scale. 1/50

date. 2026.5.14

一級建築士事務所 クロセ設計事務所

〒710-0048 岡山県倉敷市福島590-1-202 TEL 080-6348-4676

一級建築士事務所 岡山県知事登録 第14774号

一級建築士 大臣登録 第388839号 黒瀬 大貴